

WORK PORTFOLIO

SYEDA NAMEERA TAHSSEN

AIA ASSOCIATES



SESSION: 2017-2019

CONTACT: 8657652764

EMAIL: TNAMEERA@GMAIL.COM



FAIRMONT APARTMENT COMPLEX ... 9

PRESENTATION BOARDS ... 11

PROJECT WHITE BEAR ... 1



FRESENIUS MEDICAL CARE ... 5

PROJECT WHITE BEAR




PROJECT NAME: PROJECT WHITE BEAR

PROJECT AREA: 99,500 S.F.

LOCATION: 1659 PROGRESS PARKWAY, MORRISTOWN, TN 37813

OCCUPANCY: BUSINESS


SOFTWARE: REVIT 2019, LUMION

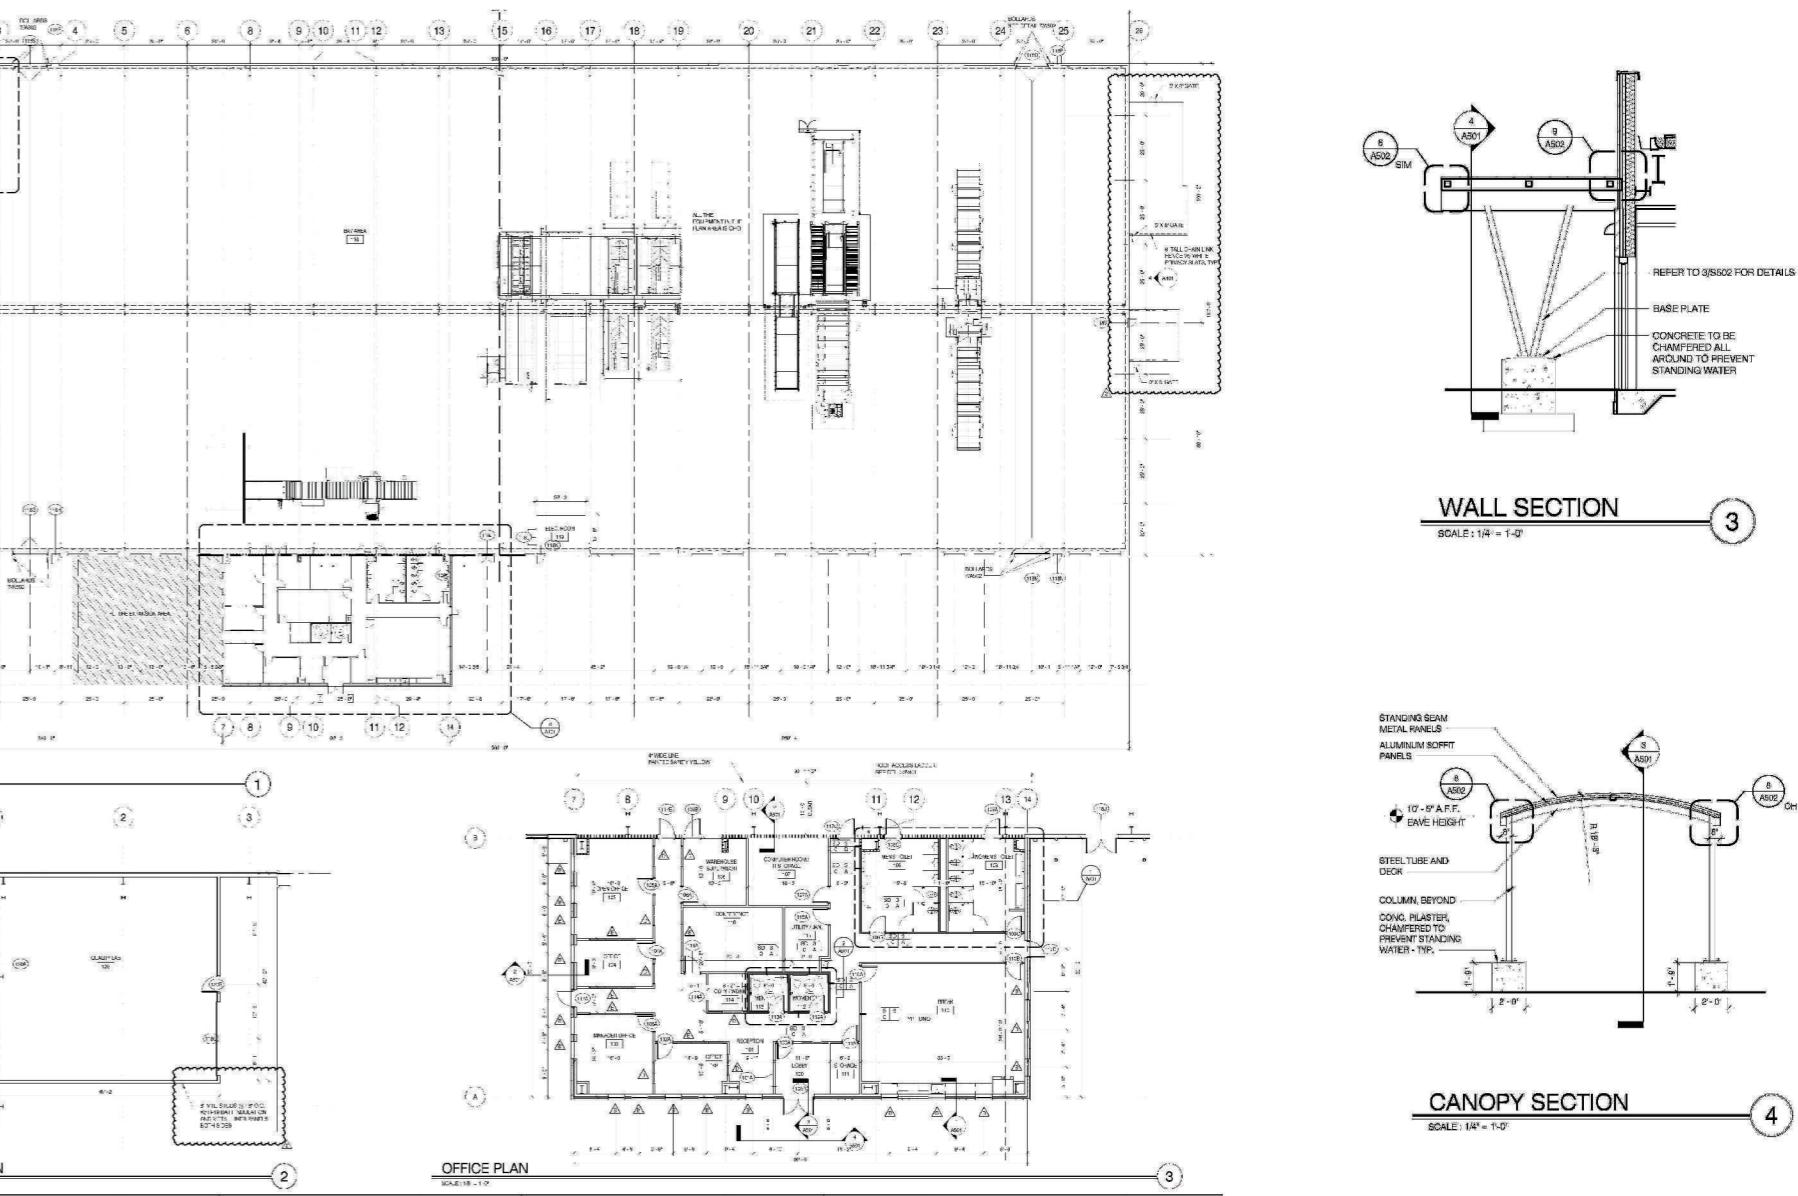


Prepared design drawings including plan, section, elevation, door details and many more. The project was done under the direct monitoring of the head of the Architecture department.

The canopy drawings and the wall detail was prepared in collaboration with the in-house structure department.

MILLWORK DETAIL

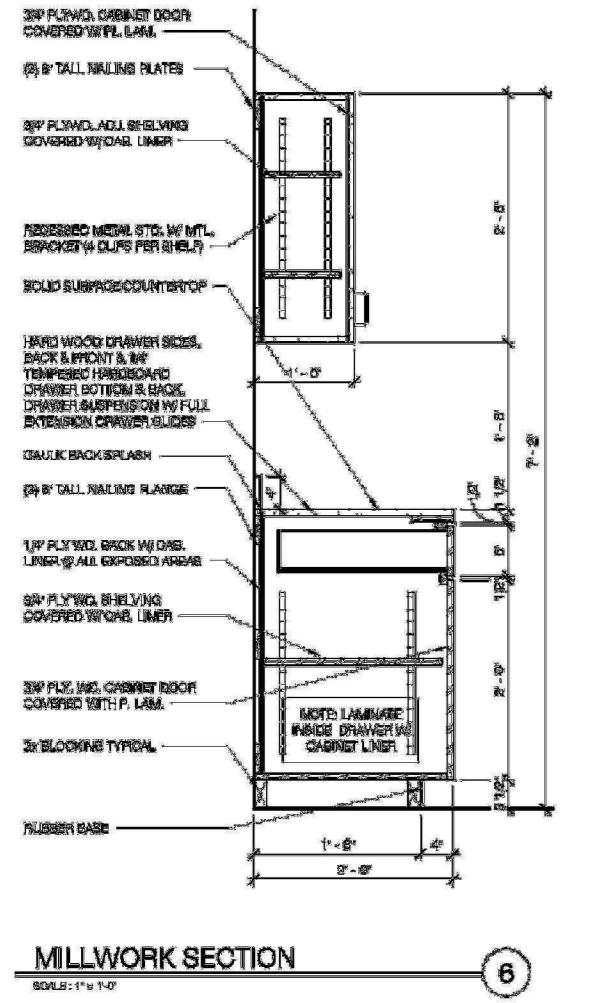

MILLWORK SECTION
SCALE: 1" = 1'-0"

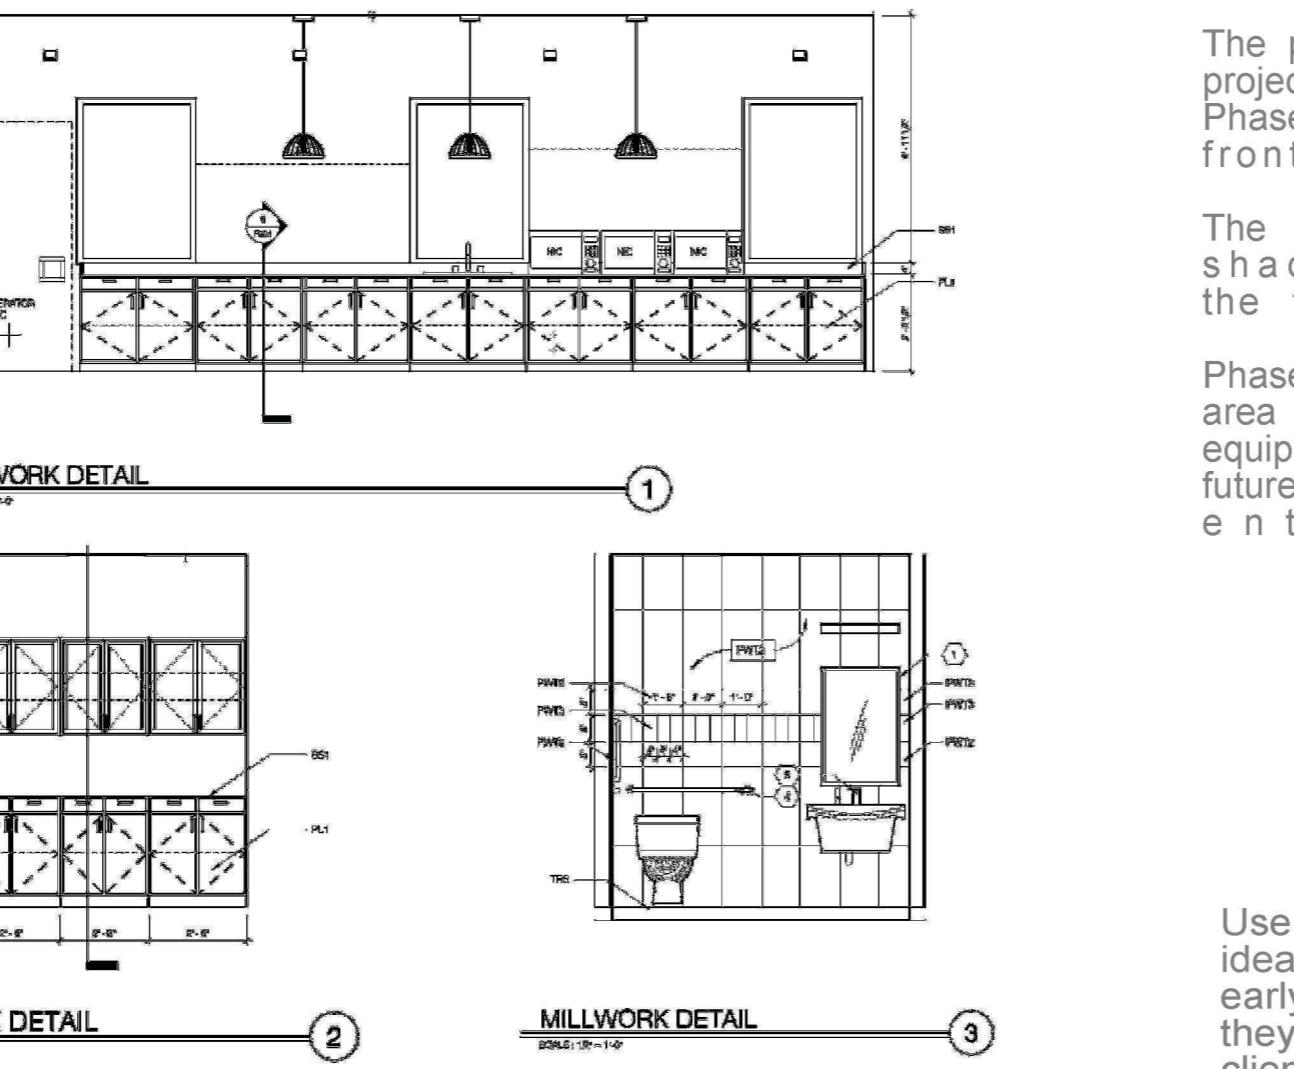

MILLWORK DETAIL
SCALE: 1" = 1'-0"

MILLWORK DETAIL
SCALE: 1" = 1'-0"

MILLWORK DETAIL
SCALE: 1" = 1'-0"

The millwork drawings were developed for better understanding the team, client and contractors. The design detail includes keynotes and dimension to avoid communication error. The style, material texture of furniture was kept simple according to clients request.

3D IMAGES


The project is a new construction project and was divided in 2 phases. Phase 1 concentrated more on the front office and Entrance.

The main entrance was shaded so that it gives the feeling of a grand entry

Phase 2 was to focus on the Bay area planning. It mainly consists of equipment, and lab area and the future expansion zone around the entrance.

Use these to develop and communicate ideas about a developing in the early stages (render process) design they might simply demonstrate to the client the ability of a particular design team to understand design.

The 3D images were rendered in Lumion. And then minor Photoshop editing was done to give it a more detailed outlook and exposure.

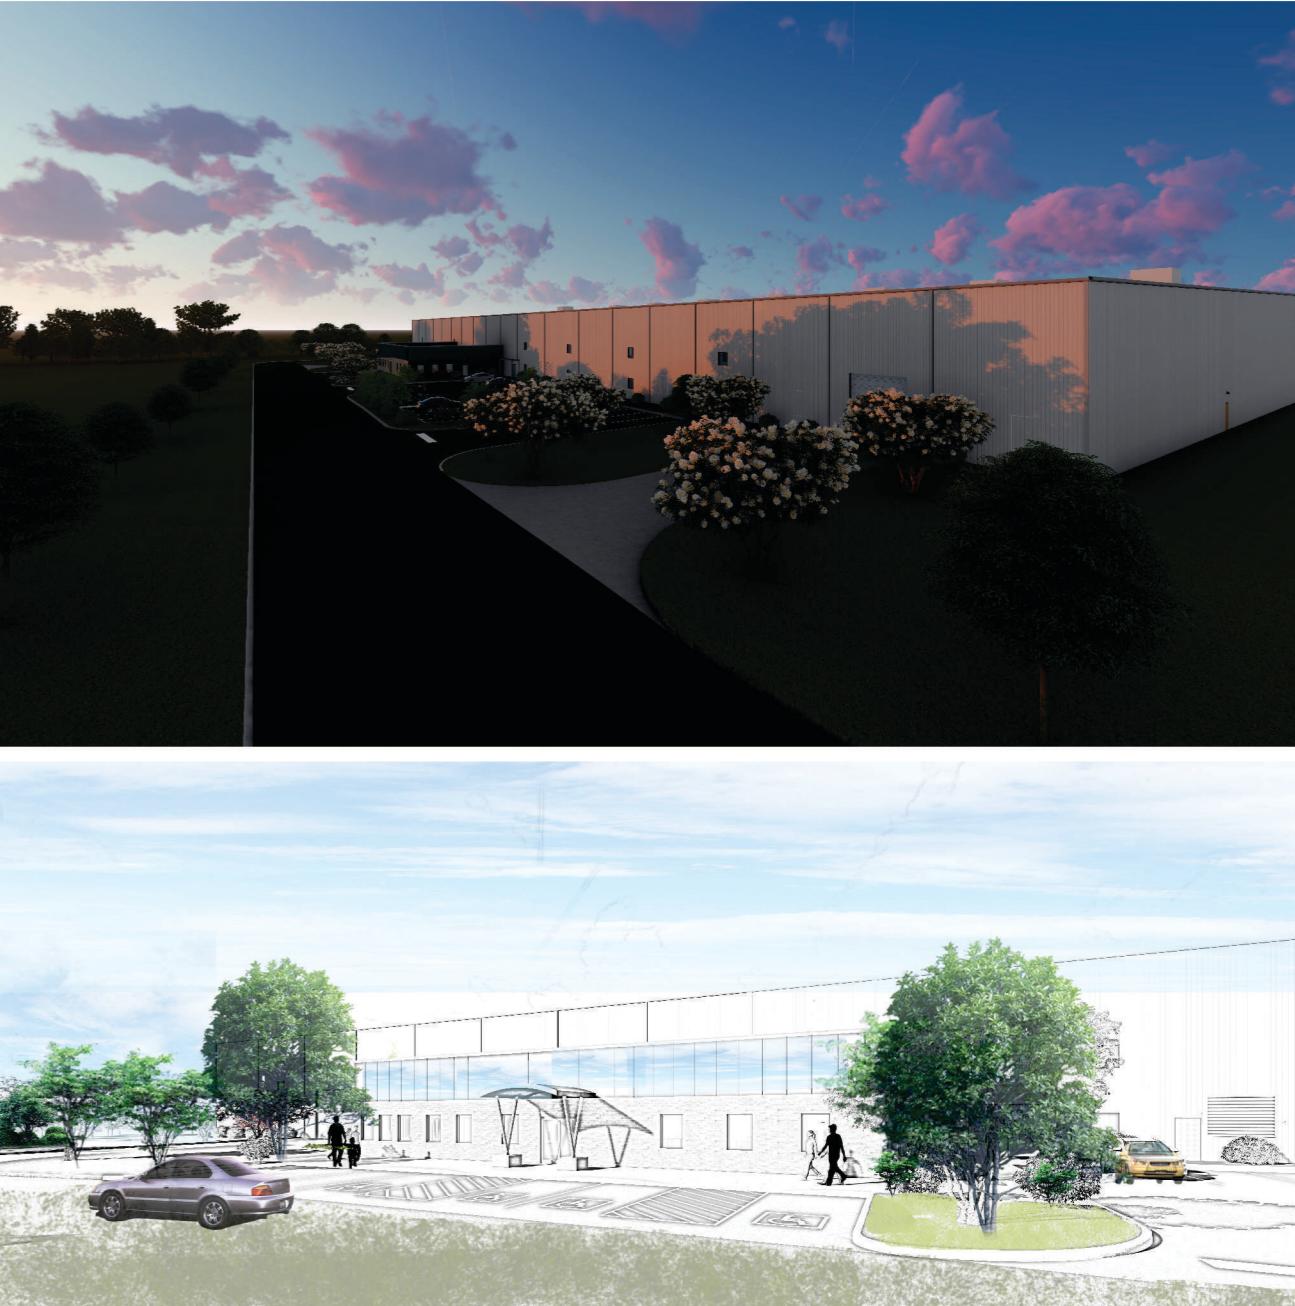

FRESENIUS MEDICAL CARE



PROJECT NAME: OFFICE RENOVATION FOR FRESENIUS MEDICAL CARE


PROJECT AREA: 10713 SQUARE FEET (Approx).

LOCATION: 5105 S NATIONAL DR, KNOXVILLE, TN 37914


OCCUPANCY: BUSINESS

SOFTWARE: REVIT 2019, AUTODESK LUMION, PHOTOSHOP


CONSTRUCTION DRAWINGS

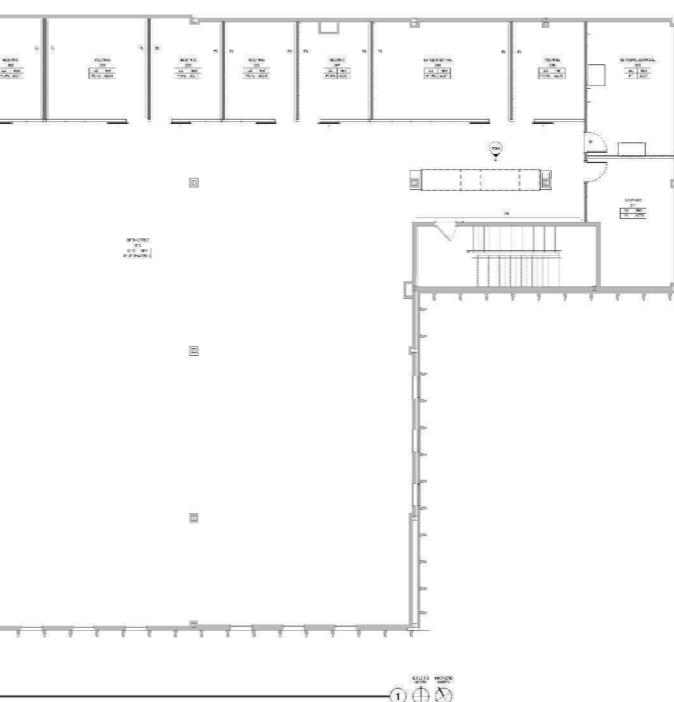

The layout design was kept simple keeping the function of the space. A gradual hierarchy of program was made in the initial layout of the office. The circulation was planned for easy movement of both the clients and the officers.

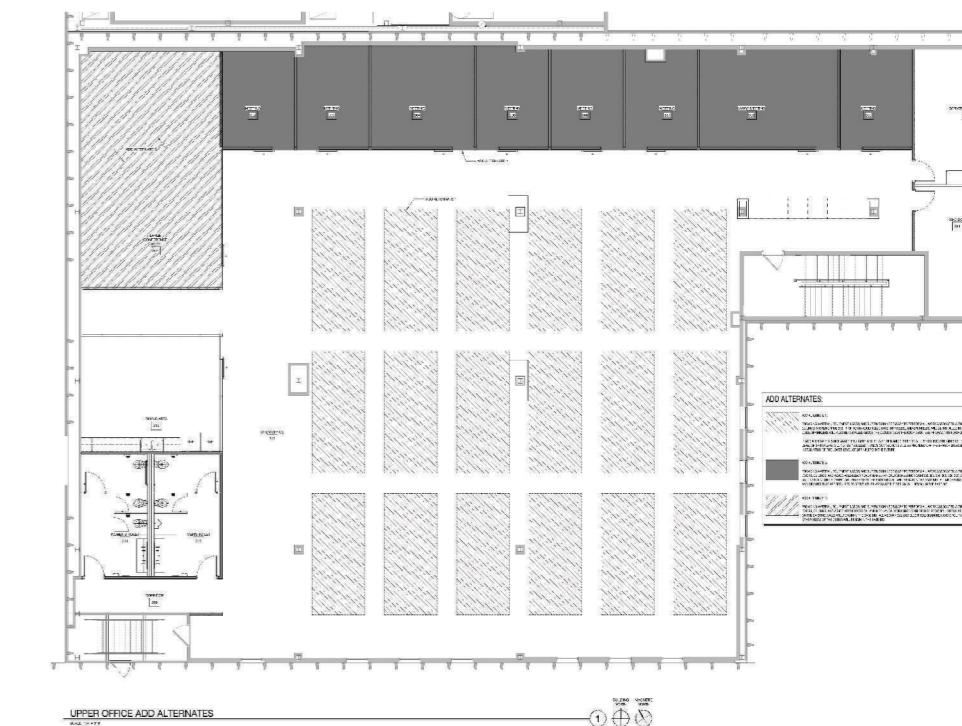

At the center the furniture layout was customized for both aesthetic and functional aspect. Lighting and other fixtures was made considering the space and its requirement.

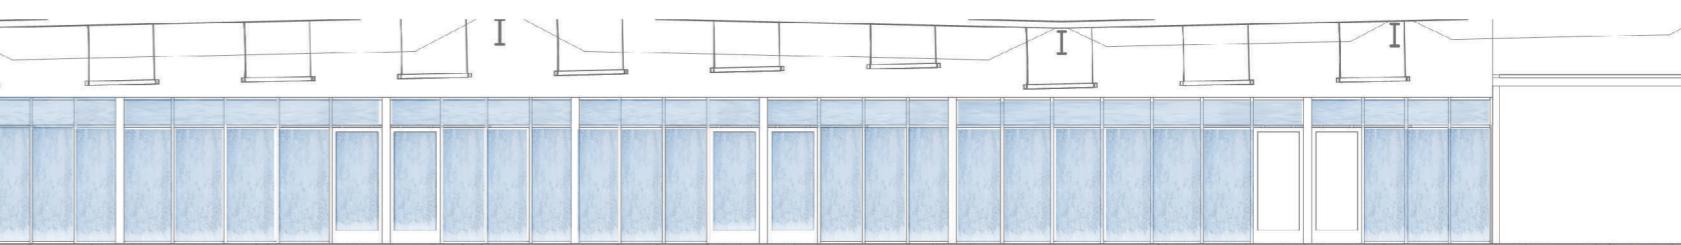


Some conceptual sketched was made during the design phase of the project. The interior spaces was given equal priority to make sure the client needs and requirement.

INTERIOR DETAIL

Studio explored the potential of both functional and emotional impacts of the interior environment to meet the need and requirements of the client.

The office design project focused on specific components of interior architecture, such as color light, material and systems of inhabitation in relation to articulating space in a more systematic order.

The main focus was to create more attractive and quality spaces for both clients and the officers here. and attract visitors to engage psychological and socio-cultural meaning as well as physical comfort, safety and performance .

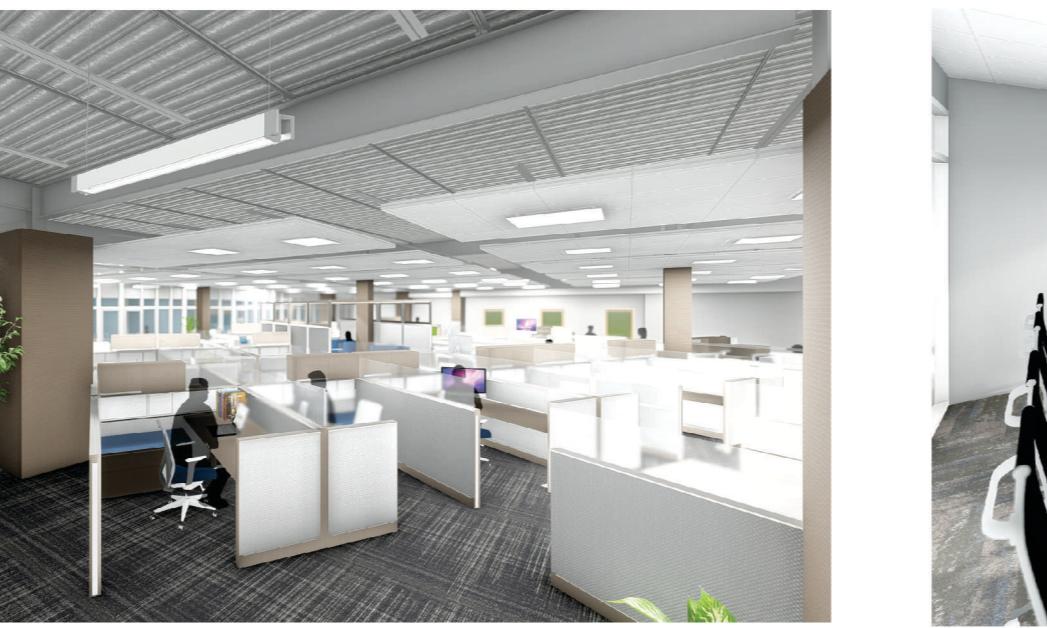

The client meetings were mostly successful because of the application of visual technology..

The community is dominated by the Hindus and by profession most of the people are shoe makers and broom makers. The people living there are very friendly, hospitable and selfless and it felt that they would do anything to hold the essence of their community.